


REV	DESCRIPTION	DATE	BY
P1	Making sketch for the prototype build plan	2026-10-01	AC

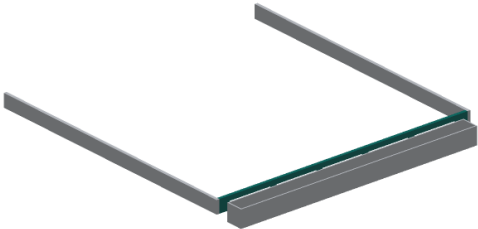

WHERE IT GOES

This part in colour, its neighbours in grey

HOW TO MAKE IT AND HOW IT FITS

Rip a strip 1,050 x 52.5 mm from 12 mm exterior plywood.

Five feed openings, one per wick strip, 33 mm tall from the bottom edge. From the centre line, the same each side (mm): middle opening 89 each side of centre; others 106 to 283; 300 to 481.

Drill a 10 mm hole in each top corner of an opening, cut down to the bottom edge with a jigsaw, file square.


The posts left between openings are about 17 mm wide, on the rib lines; handle the wall flat until it is in the frame.

Cut the stone wool liner for this wall with the same openings.

Fit: between the side walls, its bottom edge on the base ring.

The wick tails pass out through the openings to the trough.

Check: openings line up with the wick strip positions.

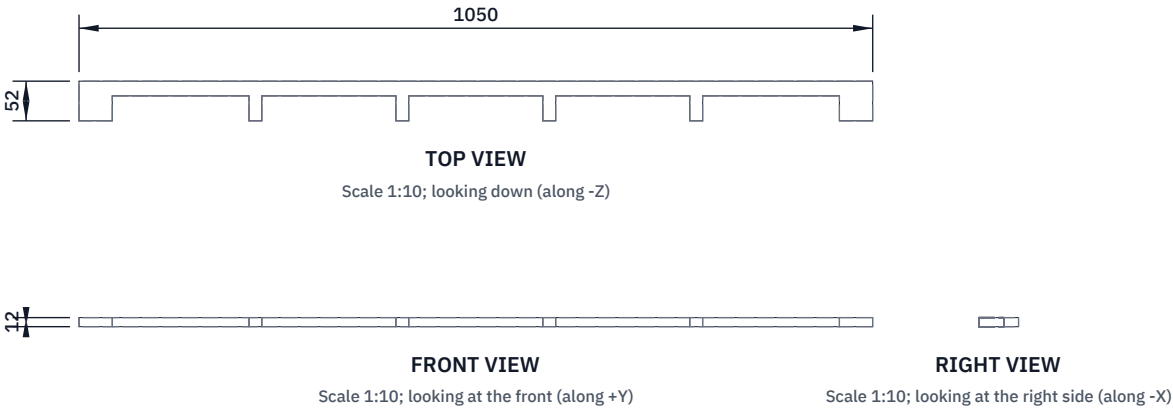

STILLSTACK			github.com/BoujeeEnjinia1701/stillstack		
StillStack high wall (feed end): making sketch					
DRAWING NO. SSK-DWG-102			REV P1	SHEET 1 of 1	SIZE ANSI B
SCALE 1:10	UNITS mm	PROJECTION 	DATE 2026-10-01		DRAWN Amish Chadha
MATERIAL / NOTES Exterior plywood 12 mm					
Licensed CERN-OHL-S-2.0 · Design Molecule Lab · designmolecule.com			Generated from cad/src; do not edit by hand		