


CONCEPT, NOT FOR FABRICATION


StillStack · github.com/BoujeeEnjinia1701/stillstack

REV	DESCRIPTION	DATE	BY
P4	Concept sheet	2026-10-01	AC

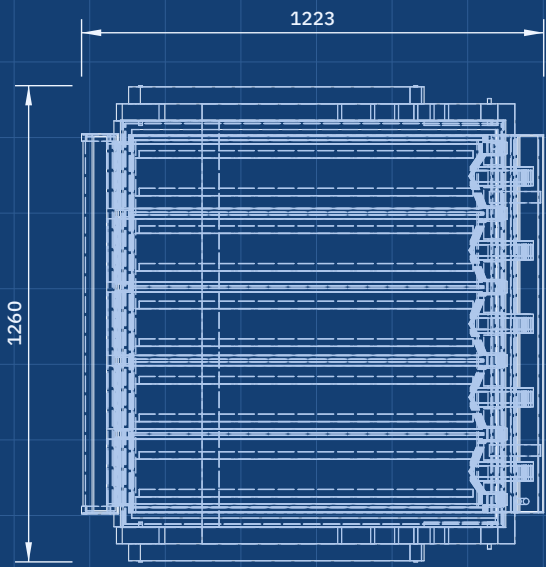


TOP VIEW

Scale 1:20; looking down (along -Z)

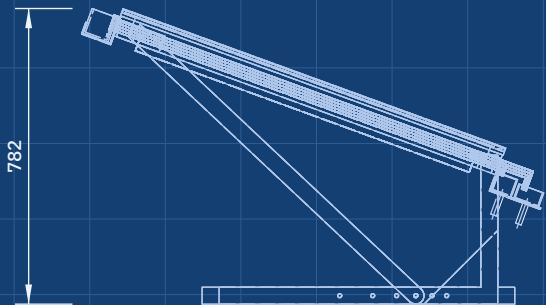


FRONT VIEW

Scale 1:20; looking at the front (along +Y)

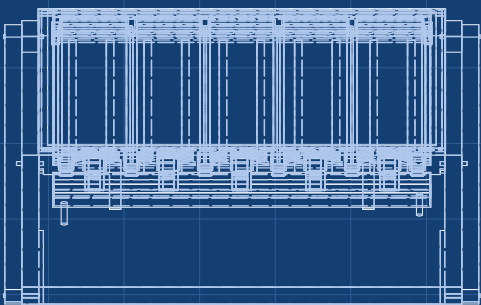


RIGHT VIEW

Scale 1:20; looking at the right side (along -X)

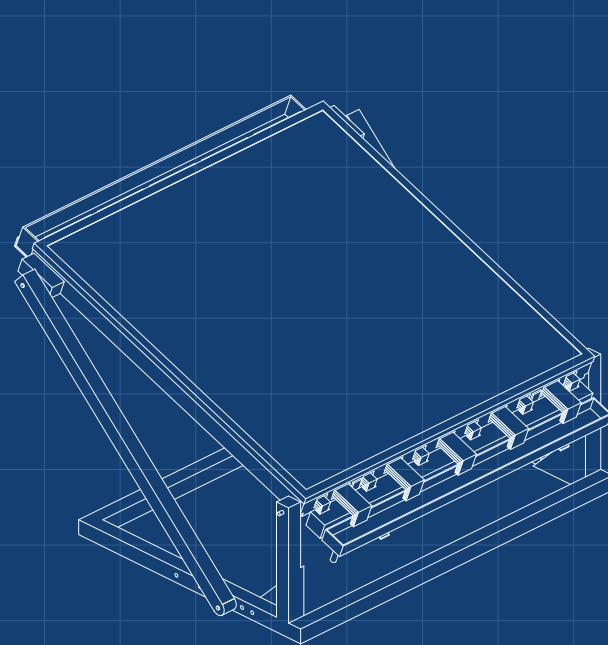

ISOMETRIC VIEW

Not to scale; grey is for scale; seen from the front right and above, about 30 deg elevation

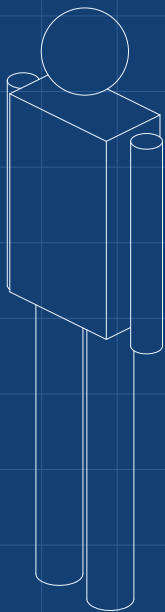

KEY FIGURES

- 1.0 m² aperture, tilt 20 deg (stand 10 to 35 deg)
- 4 stages, 6 mm vapor gaps, ribs at 194 mm
- About 10.6 L per day on 5.5 kWh/m² (SSK-CAL-001)
- Gained output ratio about 1.3
- Dry stagnation about 140 C; stages 1, 2 rated 150 C
- About USD 416 in parts (target USD 355)

STILLSTACK

github.com/BoujeeEnjinia1701/stillstack

Four-stage wick still concept

DRAWING NO. SSK-DWG-001			REV P4	SHEET 1 of 1	SIZE ANSI B
SCALE 1:20	UNITS mm	PROJECTION 	DATE 2026-10-01		DRAWN Amish Chadha
MATERIAL / NOTES Massing model for concept communication					
Licensed CERN-OHL-S-2.0 · Design Molecule Lab · designmolecule.com				Generated from cad/src; do not edit by hand	