BUILD PLAN SKETCH, PLAN NOT YET BUILT

StillStack · github.com/BoujeeEnjinia1701/stillstack

REV	DESCRIPTION	DATE	BY
P1	Making sketch for the prototype build plan	2026-10-01	AC
P2	Foot pin M10 x 120 (SSK-DEC-001 D-02)	2026-10-24	AC

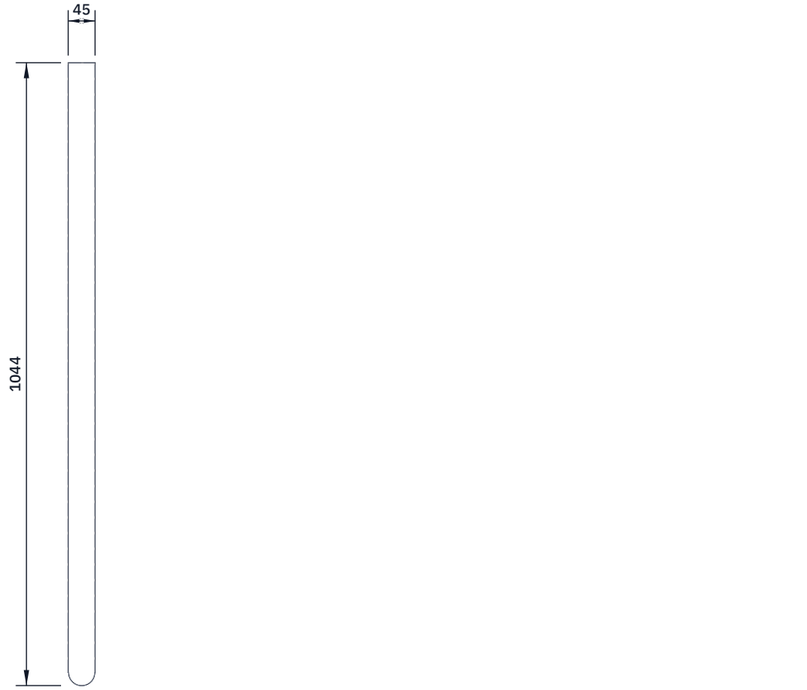

TOP VIEW

Scale 1:10; looking down (along -Z)

FRONT VIEW

Scale 1:10; looking at the front (along +Y)

RIGHT VIEW

Scale 1:10; looking at the right side (along -X)

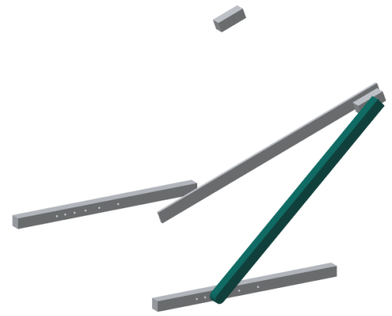

WHERE IT GOES

This part in colour, its neighbours in grey

HOW TO MAKE IT AND HOW IT FITS

Cut two lengths of 1044 mm; edges eased. Square the top end;
round the foot end to a 22 mm radius about its hole (clears the ground).
Two 10.5 mm holes through the side, 22 mm from each end:
1000 mm between centres. Drill both props clamped together.
Top: an M10 x 120 stainless bolt through the prop, the prop block
and the side wall (nut and washer inside the wall).
Foot: lies against the outside face of the ground rail; an M10
x 120 stainless bolt with a wing nut through the prop and the
rail hole for the tilt you want (and the gusset at 10 and 15 deg).
To change the tilt: support the panel, pull both foot pins, swing
the props to the new holes, refit the pins.
Check: hole centres 1,000 mm apart within 1 mm.

STILLSTACK

github.com/BoujeeEnjinia1701/stillstack

StillStack prop (make 2): making sketch

DRAWING NO.	REV	SHEET	SIZE
SSK-DWG-118	P2	1 of 1	ANSI B

SCALE	UNITS	PROJECTION	DATE	DRAWN
1:10	mm		2026-10-02	Amish Chadha

MATERIAL / NOTES

45 x 45 mm treated timber

Licensed CERN-OHL-S-2.0 · Design Molecule Lab · designmolecule.com

Generated from cad/src; do not edit by hand