



CONCEPT, NOT FOR FABRICATION


REV	DESCRIPTION	DATE	BY
P1	Concept sheet	2026-09-24	AC

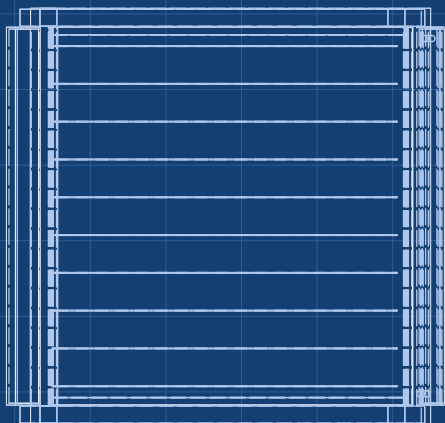


TOP VIEW
Scale 1:20

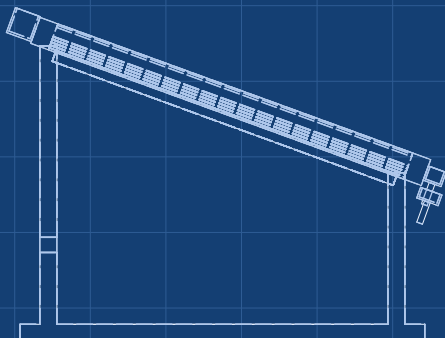

FRONT VIEW
Scale 1:20

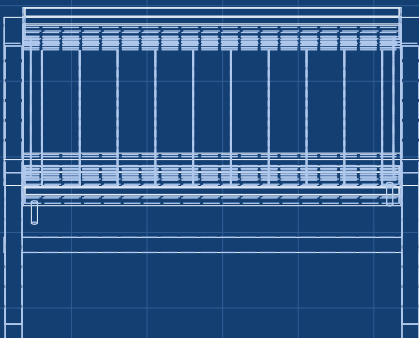

RIGHT VIEW
Scale 1:20

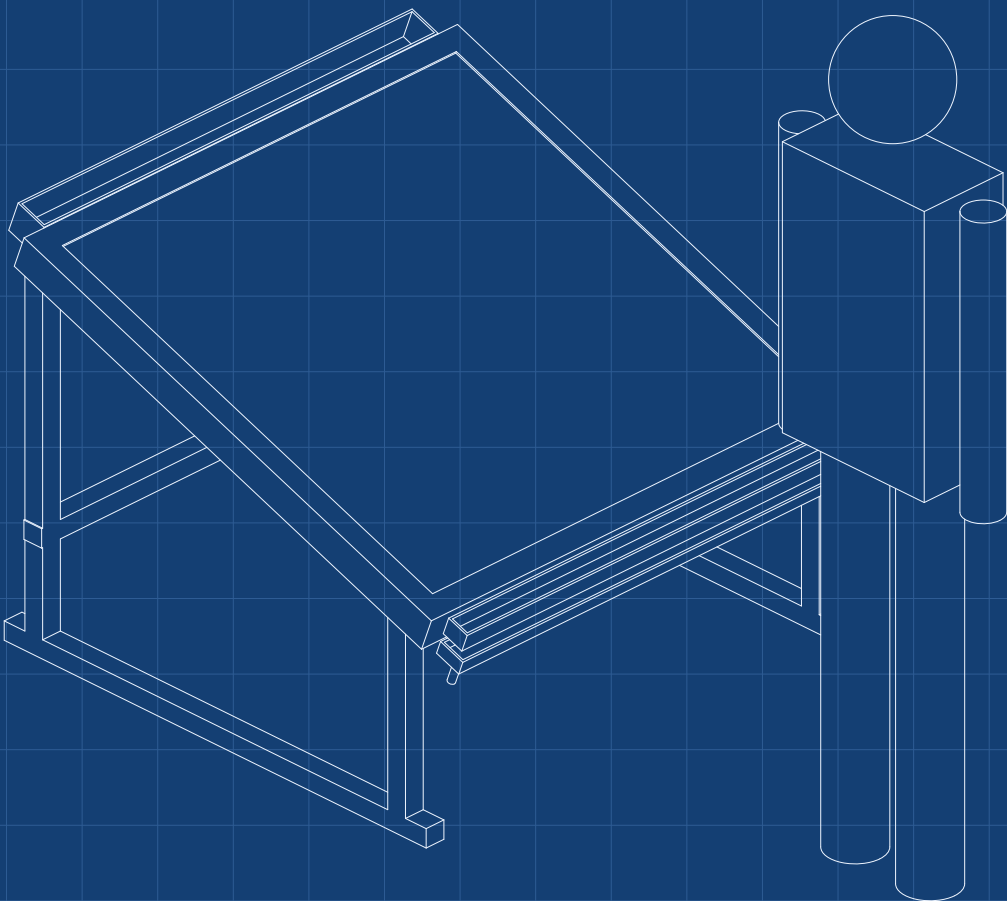

ISOMETRIC VIEW
Not to scale; figure is a 1.75 m person

KEY FIGURES

1.0 m² aperture, tilted 20 deg
4 stages, 6 mm vapor gaps
About 13 L per day on 5.5 kWh/m² (estimate)
Single stage: about 3.8 L per day (estimate)
Gained output ratio about 1.5 (estimate)
About \$240 in parts (indicative)

STILLSTACK

Four-stage wick still concept

DRAWING NO.

SSK-DWG-001

REV

P1

SHEET

1 of 1

SIZE

ANSI B

SCALE

1:20

UNITS

mm

PROJECTION



DATE

2026-09-24

DRAWN

Amish Chadha

MATERIAL / NOTES

Massing model for concept communication