



CONCEPT, NOT FOR FABRICATION


REV	DESCRIPTION	DATE	BY
P2	Concept sheet	2026-09-25	AC

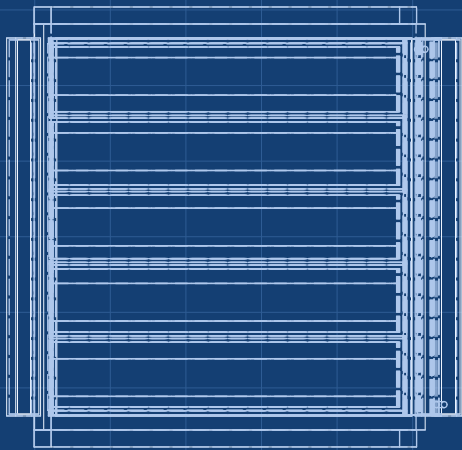


TOP VIEW
Scale 1:20

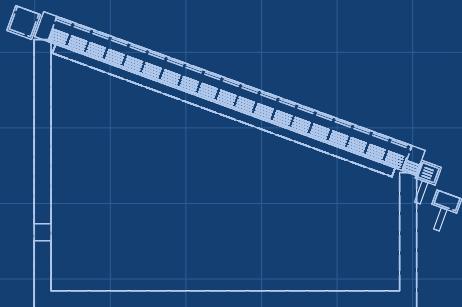


FRONT VIEW
Scale 1:20

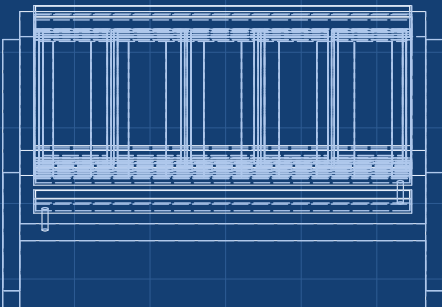

RIGHT VIEW
Scale 1:20

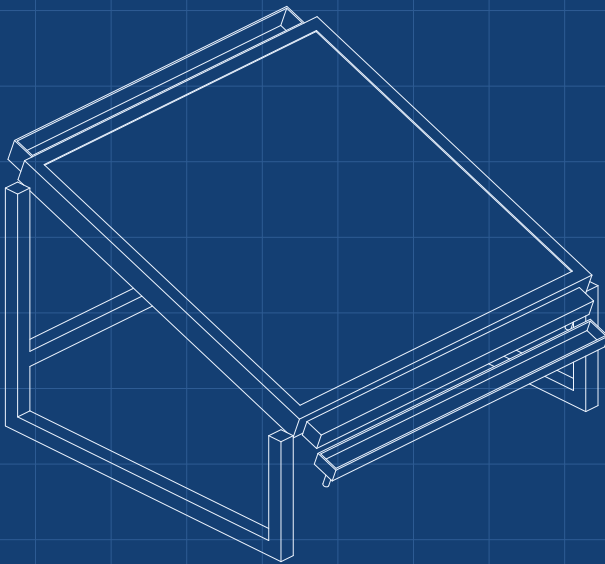

ISOMETRIC VIEW
Not to scale; grey is for scale

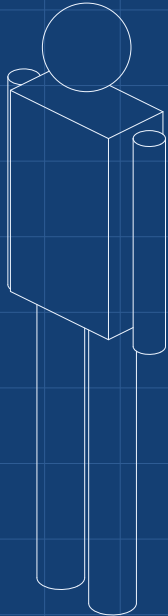

KEY FIGURES

1.0 m2 aperture, tilt 20 deg (stand 10 to 35 deg)
4 stages, 6 mm vapor gaps, ribs at 194 mm
About 10.6 L per day on 5.5 kWh/m2 (SSK-CAL-001)
Gained output ratio about 1.3
Dry stagnation about 140 C at stage 1
About \$317 in parts (indicative; budget \$250)

STILLSTACK

Four-stage wick still concept

DRAWING NO. SSK-DWG-001			REV P2	SHEET 1 of 1	SIZE ANSI B
SCALE 1:20	UNITS mm	PROJECTION 	DATE 2026-09-25	DRAWN Amish Chadha	

MATERIAL / NOTES
Massing model for concept communication